


Stückliste

Pos. Nr.	Stück je Kette	Benennung	Código Elecnor
1	2	Traggelenk DIN VDE 0212-466-A25x130-22-100	KBE-770F-22
2	2	Gabellasche DIN VDE 0212-478-A22-24 BH: 150	B251014A06
3	2	Doppelöse D22 BH: 120 SAB Anschlag 41 GER	KBE-712-29A-41
4	12	Verbindungsbolzen DIN VDE 0212-473-22x57-8.8	WN005A08
5	8	Schutzring Einhorn Verbund oben BH: 270	B351017
6	2	Isolator Verbund CS210 2900/1200 S22	3FL7 088-3MM41-1XX9
7	2	Doppelöse C22 BH: 120 SAB Anschlag 41	KBE-712-28A-41
8	1	Abstandhalter A22-22-250/125 3eck	KBE-704-94
9	5	Doppelöse B22 BH: 90	8415513
10	1	Abstandhalter A32-22-400/100 3eck	KBE-704-600
11	2	Doppelöse DIN VDE 0212-469-B32 BH:140	B232016
12	2	Abstandhalter E22-32-600/600 Rahmen	B221029
13	8	Doppelöse DIN VDE 0212-469-D22 BH:120 SAB	B234007
14	4	Isolator Verbund CS260 7600/2600 S22	3FL8 308-3FF61-7XX9
15	4	Schutzring Einhorn Verbund unten BH: 300	B353008
16	2	Abstandhalter F22-600/400/720 Trapez-Gar	B226004
17	4	Spannschloß DIN VDE 0212-434-B22 M27x420-580	B261008A02
18	4	Keilabspannklemme S22 32,2-32,9	B119040A06
19	4	Stromschlaufen-Distanzhalter 2-BDL 32,0-33,4	409033/2/400/Z
20	8	Endhülse 32,5-33,1 AL	110617
21	2	Leiterseil 565-AL1/72-ST1A (Finch)	-

Beachtung bei der Montage / Mengenermittlung

- 1) Verbindungsbolzen: Mutter und deren Sicherungen zum Mastschaft, zur niedrigeren Mastnummer oder nach unten
- 2) Montage der Bauteile nach Herstellervorschrift
- 3) Montage der A2/A4 - Schraubenverbindungen gefettet
- 4) Pos. 1: Größe Traggelenk anpassen an Mastkonstruktion
- 5) Pos. 21: Länge Leiterseil an Stromschlaufe anpassen

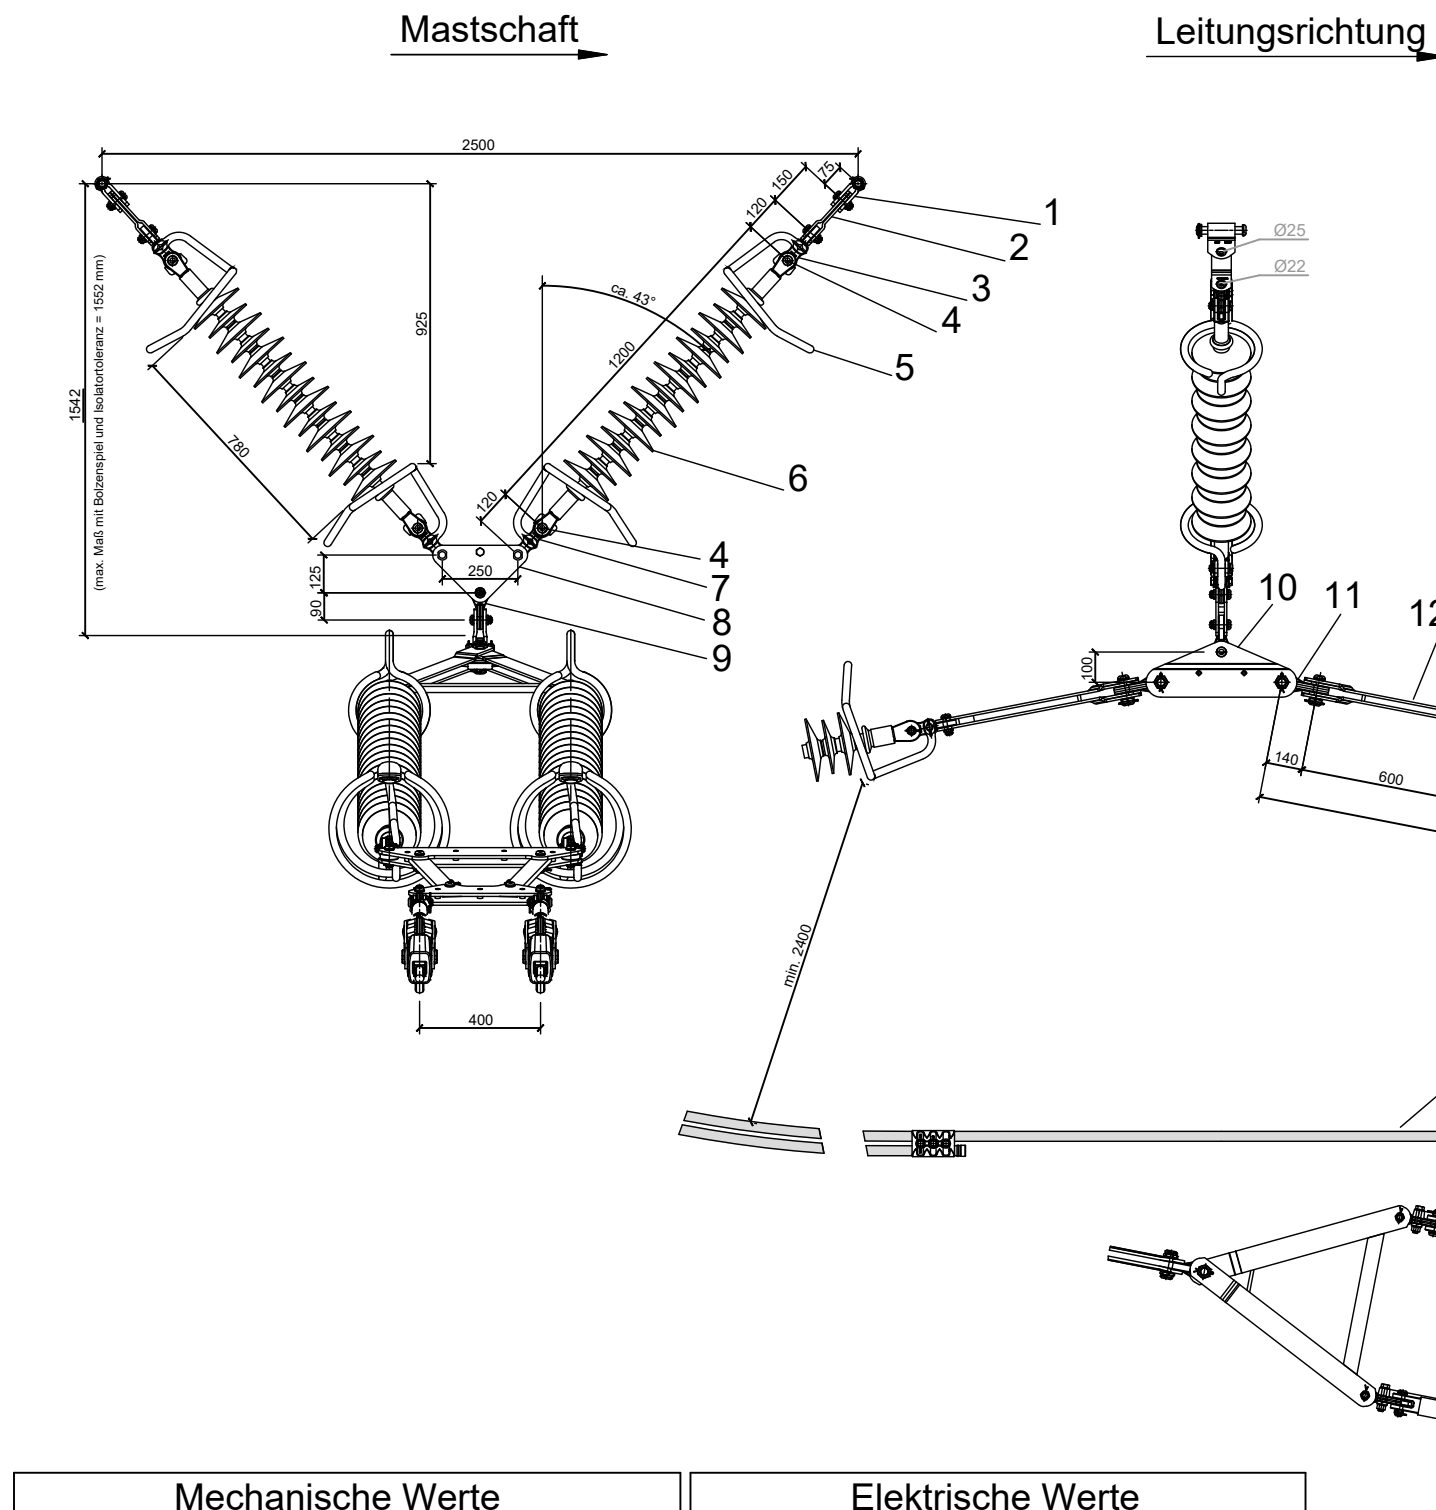

Mechanische Werte		Elektrische Werte	
Kettengewicht:	ca. 430 kg	Bemessungs-Kurzzeitstrom:	40 kA
Kettenlänge Tragteil:	ca. 1550 mm	Schlagweite:	2930 mm
Kettenlänge Abspannteil:	ca. 5400 mm	Isolator:	Verbund-Longstabilisolator
Kettenfläche:	ca. 4,4 m²	Ausführungsform 1:	CS210 C22L 500/2900/1200
Öffnungswinkel:	ca. 86°	Ausführungsform 2:	CS260 C22L 1300/7600/2600
max. Lastwinkel:	ca. 45,5°	Kriechweg:	min. 10500 mm
Leiter/ $\sigma_{+10^{\circ}\text{C}}$:	2x565-AL1/72-ST1A / 58 $\frac{\text{N}}{\text{mm}^2}$	Verschmutzungsgrad:	III nach DIN EN 60071-2:1997
Leiterdurchmesser:	32,85 mm	SPS-Klasse:	d nach IEC 60815
Eislastzone / Windzone:	E2/W4		
Gewichts-/Windspannweite:	650/550 m		

a	15.12.2025	Penning	Bezug auf Mastnummer 152 entfernt.		
Index	Ausgabedatum	Name	Änderung		
Techn. Referenz AMG-AC-OL Dörr		erstellt von GFG-DD-DO Aschenbrenner	geprüft von GFG-ON-SL Alex Schmidt		Erstelldatum 16.01.2024
Eigentümer der Zeichnung Tennet Taking power further		Zugehörigkeit Entwurfsplanung			Format A3-Q
		Dokumentenart Anordnungszeichnung			Maßstab 1:20
		Status Freigegeben			Ausgabedatum 15.12.2025
Identnummer 002-294-203		Titel Kettenzeichnung 380-kV_TA-Kette V-Teil_2x565-AL1/72-ST1A_Verbund_SPSd 380-kV Audorf_Süd - Handewitt		Objekt LH-13-305	
				Fremdnummer	Blatt