


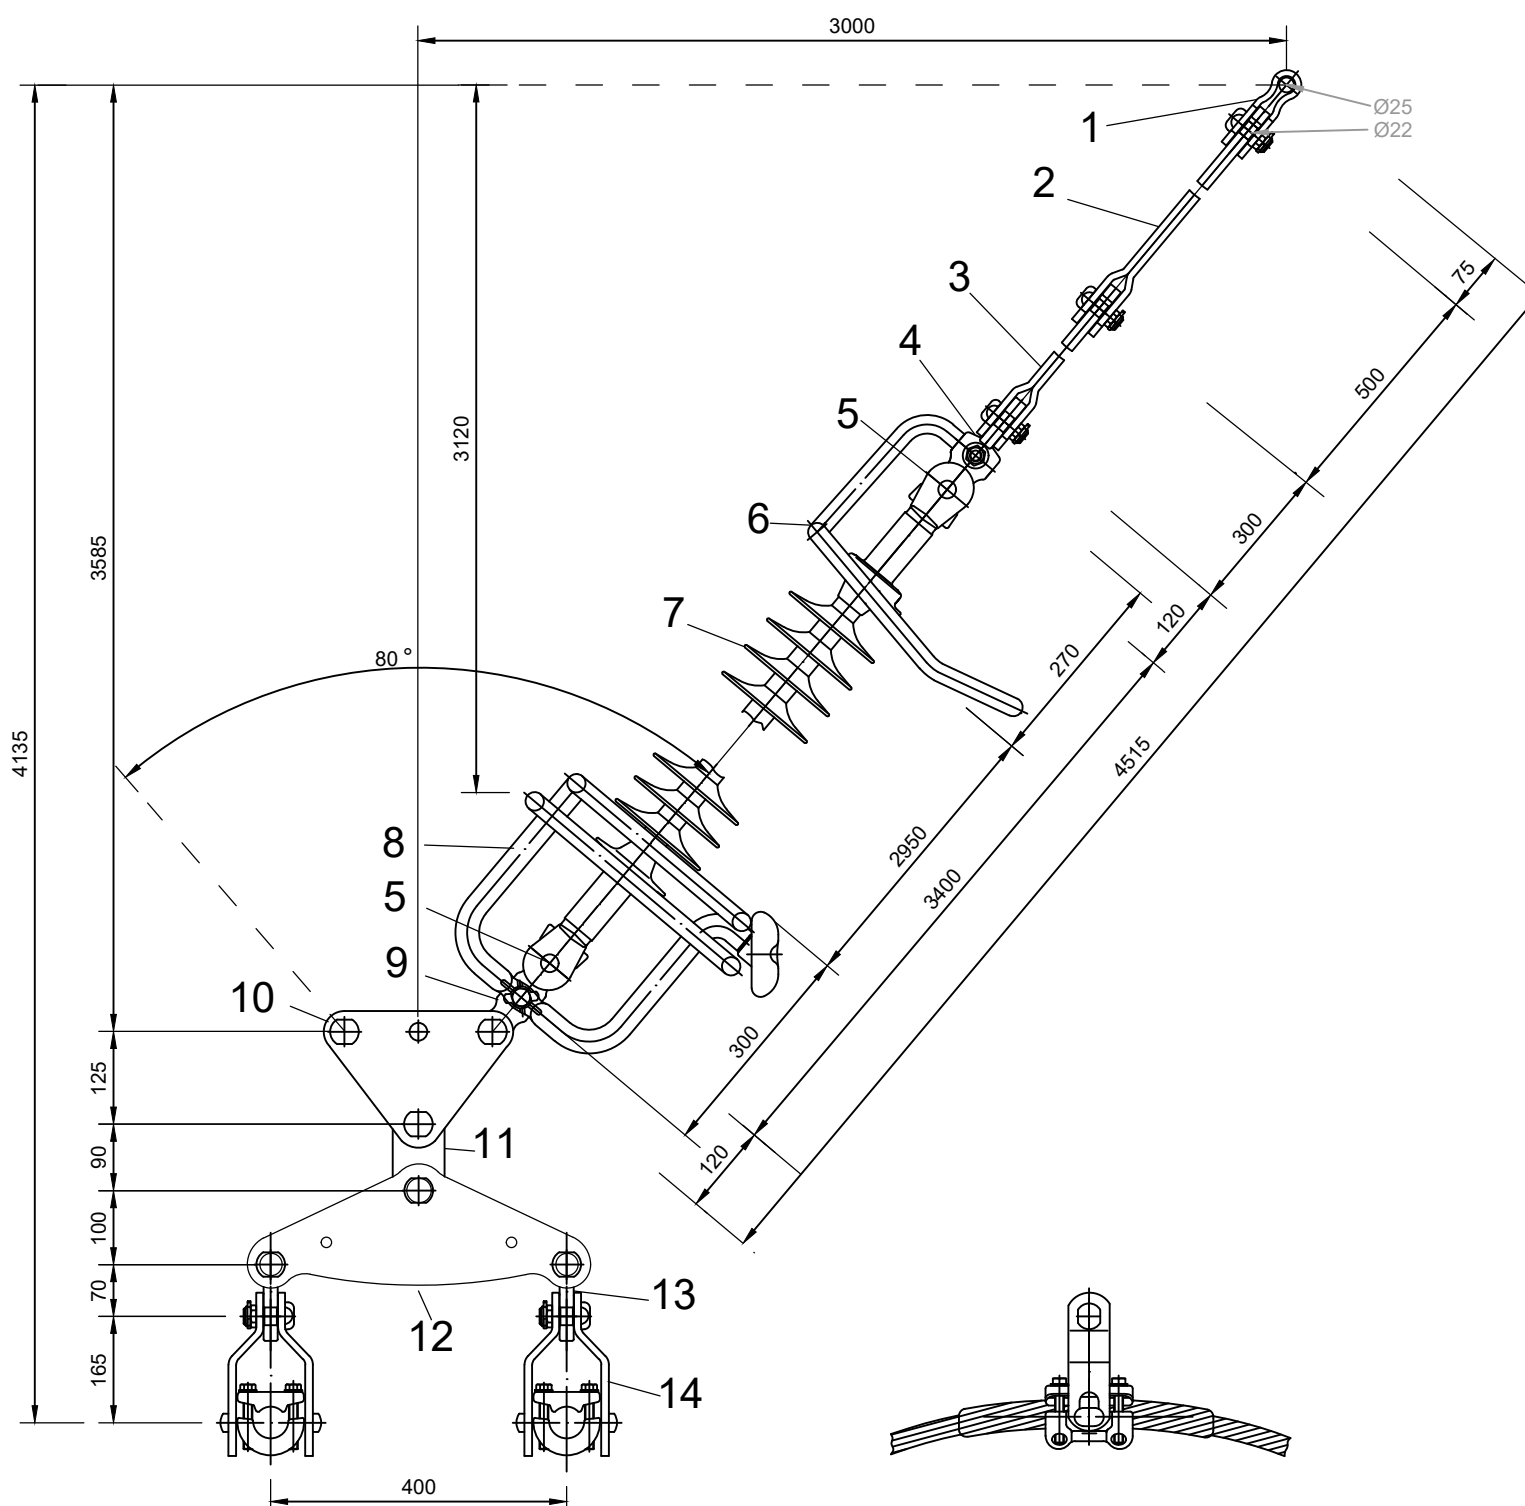

# Stückliste

| Pos. Nr. | Stück je Kette | Benennung                                          | Código Elecnor      |
|----------|----------------|----------------------------------------------------|---------------------|
| 1        | 2              | Traggelenk DIN VDE 0212-466-A25x130-22-100         | 5 KBE-770f-22       |
| 2        | 2              | Gabellasse DIN VDE 0212-478-A22-24 BH: 500         | B251014A19          |
| 3        | 2              | Gabellasse DIN VDE 0212-478-A22-24 BH: 300         | B251014A15          |
| 4        | 2              | Doppelöse D22 BH: 120 SAB Anschlag 41 GER          | KBE-712-29A-41      |
| 5        | 4              | Verbindungsbolzen DIN VDE 0212-473-22x57-8.8       | WN005A08            |
| 6        | 2              | Schutzring Einhorn Verbund oben BH:270             | B351017             |
| 7        | 2              | Isolator Verbund CS260 10500/3400 S22              | 3FL8 308-3FF61-7XX9 |
| 8        | 2              | Schutzring Tandem Verbund unten BH:300             | B353008             |
| 9        | 2              | Doppelöse C22 BH: 120 SAB Anschlag 41              | KBE-712-28A-41      |
| 10       | 1              | Abstandhalter DIN VDE 0212-470-A22-22-250/125 3eck | KBE-704-94          |
| 11       | 1              | Doppelöse A22 BH: 90                               | 8431551             |
| 12       | 1              | Abstandhalter DIN VDE 0212-470-A19-22-400/100 3eck | B211069             |
| 13       | 2              | Doppelöse DIN VDE 0212-469-B19 BH:70               | F06022/ 210205      |
| 14       | 2              | Spiraltragklemme S19 32,25-33,69                   | 407007A/32,85       |

## Mechanische Werte

|                           |                                         |
|---------------------------|-----------------------------------------|
| Kettengewicht:            | ca. 135 kg                              |
| Kettenlänge:              | ca. 4150 mm                             |
| Kettenfläche:             | ca. 0,3 m²                              |
| Öffnungswinkel:           | ca. 80°                                 |
| max. Lastwinkel:          | 42,5°                                   |
| Leiter/σ +10°C:           | 2x565-AL1/72-ST1A / 59 $\frac{N}{mm^2}$ |
| Leiterdurchmesser:        | 32,85 mm                                |
| Eislastzone /Windzone:    | E2/W4                                   |
| Gewichts-/Windspannweite: | 700/550 m                               |

## Elektrische Werte

|                           |                              |
|---------------------------|------------------------------|
| Bemessungs-Kurzzeitstrom: | 40 kA                        |
| Schlagweite:              | 2950 mm                      |
| Isolator:                 | Verbund-Longstabisolator     |
| Ausführungsform:          | CS260 1675/10500/3400        |
| Kriechweg:                | min. 10500 mm                |
| Verschmutzungsgrad:       | III nach DIN EN 60071-2:1997 |
| SPS-Klasse:               | d nach IEC 60815             |

## Beachtung bei der Montage / Mengenermittlung

- 1) Verbindungsbolzen: Mutter und deren Sicherungen zum Mastschaft, zur niedrigeren Mastnummer oder nach unten
- 2) Brennstrebe: nach außen
- 3) Montage der Bauteile nach Herstellervorschrift
- 4) Montage der A2/A4 - Schraubenverbindungen gefettet
- 5) Pos.1: Traggelenk eventuell anpassen an Mastkonstruktion
- 6) Einbau und Anzahl gemäß Schwingungsstudie

| Index   | Ausgabedatum | Name                                 | Änderung                                 |
|---|--------------|--------------------------------------|------------------------------------------|
| Techn. Referenz<br>AMG-AC-OL<br>Dörr                                                                              |              | erstellt von<br>GFG-DD-DO<br>Penning | geprüft von<br>GFG-ON-SL<br>Alex Schmidt |
| Eigentümer der Zeichnung<br> |              | Zugehörigkeit<br>Entwurfsplanung     | Erstelldatum<br>15.12.2025               |
| Dokumententart<br>Anordnungszeichnung                                                                             |              | Status<br>Freigegeben                | Format<br>A3-Q<br>Maßstab<br>-           |
| Titel<br>Kettenzeichnung<br>380-kV_V-Kette_2x565-AL1/72-ST1A_Verbund_SPSd<br>380-kV Audorf_Süd - Handewitt        |              | Objekt<br>LH-13-305                  | Ausgabedatum<br>15.12.2025               |
| Identnummer<br>002-442-214                                                                                        |              | Fremdnummer                          | Blatt                                    |