


LH-13-305  
Audorf/Süd – Handewitt

Seiltyp:  
ASLH-DS(S)BB 1x48 SMF  
(92-AL3/49-A20SA-10,2)

PLANUNGSSTAND

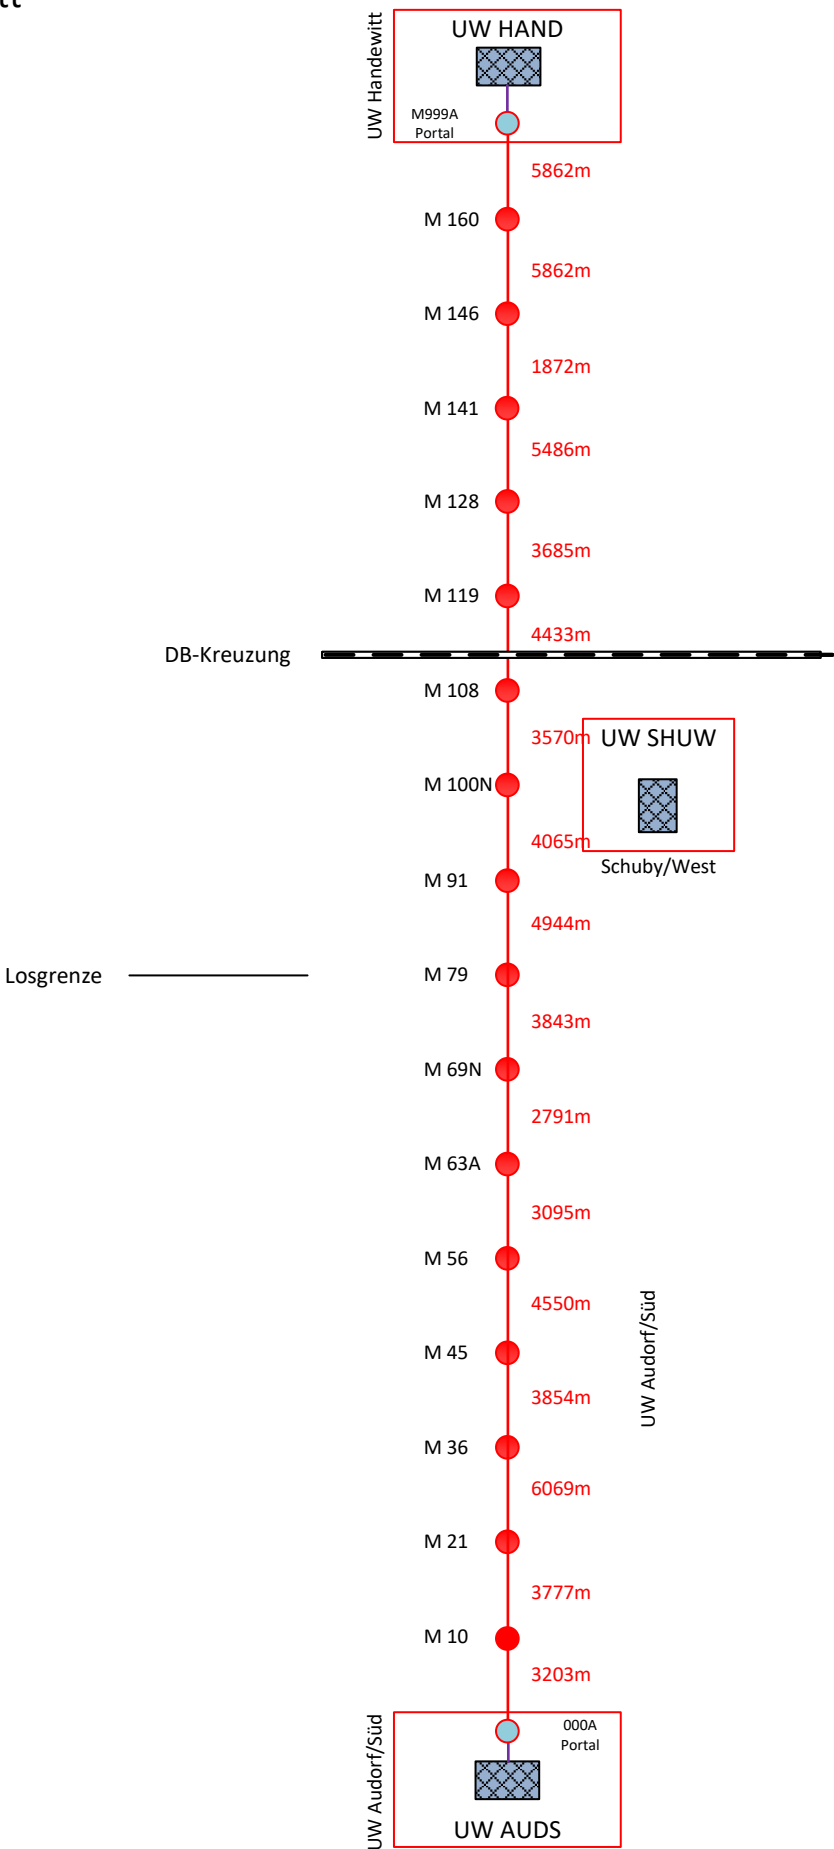

Legende

380

220

110

kV

Portal

Mast ohne Muffe

Muffenmast

OPGW

LWL Erdkabel

LWL Hybridkabel

Geplant

andere Betreiber

Betriebsgebäude

EK: 4X12 E9/125  
Steckertyp E2000/8°



|                                                                                       |  |               |                                                  |            |                            |
|---------------------------------------------------------------------------------------|--|---------------|--------------------------------------------------|------------|----------------------------|
| Erstellt durch<br>Torsten Runge                                                       |  | Genehmigt von |                                                  | Sachnummer |                            |
| Titel, Zusätzlicher Titel<br>LH-14-305<br>UW Audorf/Süd - Handewitt<br>LWL-Muffenplan |  |               | Dokumentenart<br>CIA3 – Confidential Information |            |                            |
|                                                                                       |  |               | Maßstab<br>kein                                  | Änd.<br>3  | Ausgabedatum<br>10.04.2025 |