


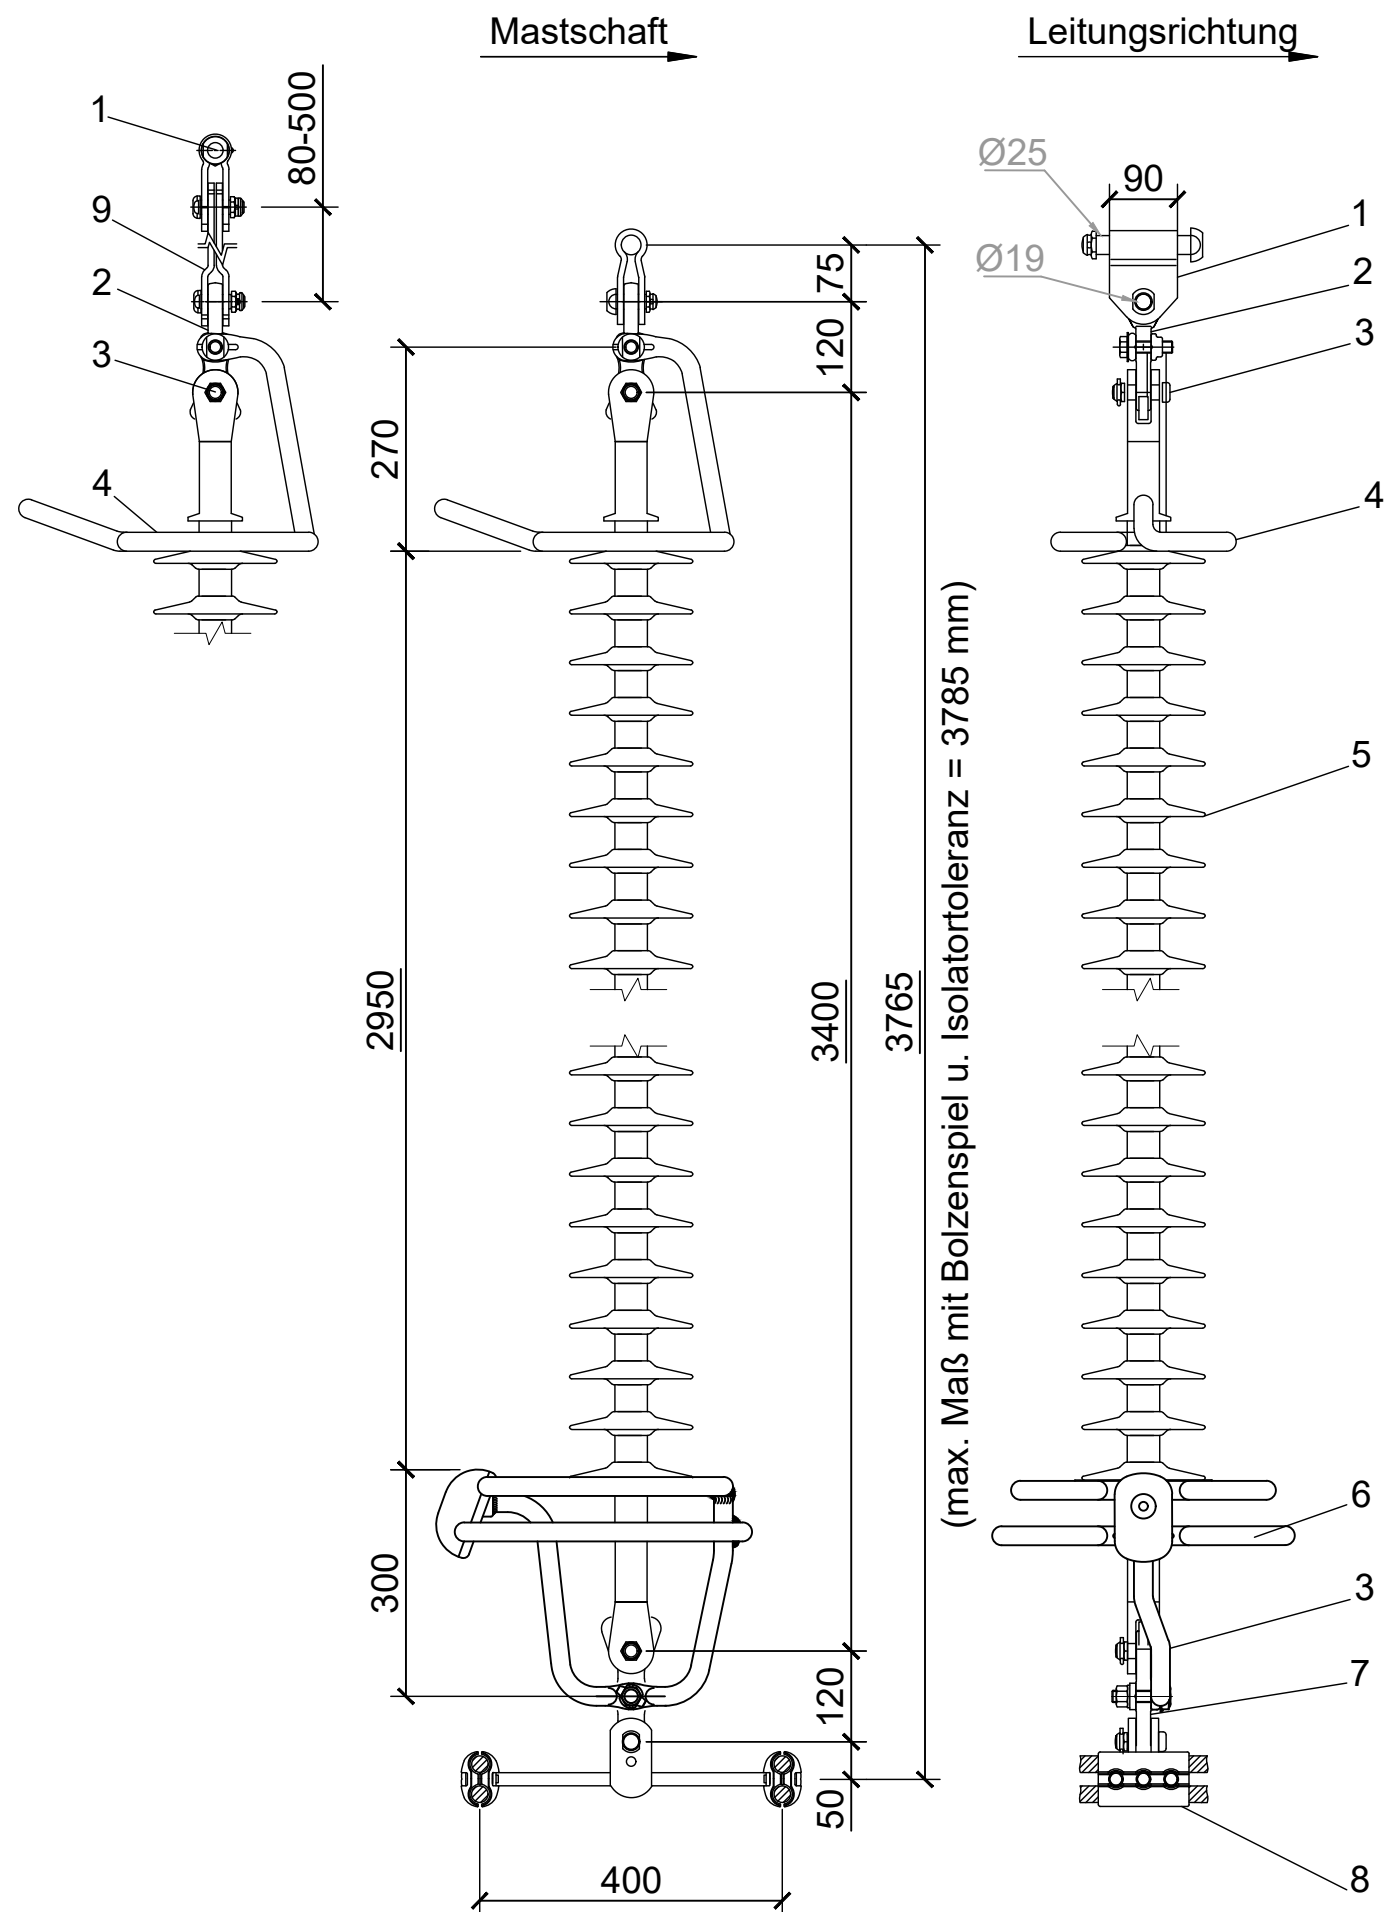

Stückliste

Pos. Nr.	Stück je Kette	Benennung	Nennkraft in kN	SAP - Nummer
1	1	Traggelenk DIN VDE 0212-466-A25X130-19-100 5)	200	52231510
2	1	Doppelöse D19 BH: 120 SAB Anschlag 36 GER	200	52219751
3	2	Verbindungsbolzen DIN VDE 0212-473-19X48-8.8	-	52232604
4	1	Schutzring Einhorn Verbund oben BH: 270	-	52201011
5	1	Isolator Verbund CS160 8400/3400 S19	160	52105323
6	1	Schutzring Tandem Verbund unten BH: 300	-	52201012
7	1	Doppelöse C19 BH: 120 SAB Anschlag 36	200	52219744
8	1	Stromschlaufendistanzhalter m. Gabelanschluss 2 BDL 32,0-33,4	-	-
9	1	Gabellasse DIN VDE 0212-478-A19-20 BH:80...500 6)	200	siehe Liste

Mechanische Werte

Kettengewicht:	ca. 45 kg
Kettenlänge:	ca. 3780 mm
Kettenfläche:	ca. 0,3 m²
Leiter:	2x565-AL1/72-ST1A
Leiterdurchmesser:	32,85 mm

Elektrische Werte

Bemessungs-Kurzzeitstrom:	40 kA
Schlagweite:	2950 mm
Isolator:	Verbund-Langstabisolator
Ausführungsform:	CS160 C19L 1675/8400/3400
Kriechweg:	8400 mm
Verschmutzungsgrad:	II nach DIN EN 60071-2: 1997
SPS-Klasse:	c nach IEC 60815

Beachtung bei der Montage / Mengenermittlung

- 1) Verbindungsbolzen: Mutter und deren Sicherungen zum Mastschaft, zur niedrigeren Mastnummer oder nach unten
- 2) Brennstrebe: vom Mastschaft weg
- 3) Montage der Bauteile nach Herstellervorschrift
- 4) Montage der A2/A4 - Schraubenverbindungen gefettet
- 5) Pos. 1: Größe Traggelenk anpassen an Mastkonstruktion
- 6) Pos. 9: Länge Gabellasse anpassen an Winkelstellung/Schlaufenführung

Index	Ausgabedatum	Name	Änderung
Techn. Referenz AMT-AT-CL-LG Dörr	erstellt von GFO-G-PM-DTL Penning	geprüft von AMT-AT-CL-LG Dörr	Erstelldatum 13.11.2024 Format A3-Q Maßstab 1:10
Eigentümer der Zeichnung 	Zugehörigkeit Standard	Dokumentenart Anordnungszeichnung	Status Freigegeben
Identnummer 002-384-768	Titel Kettenzeichnung 380-kV_EH-Kette_SSDH_2x565-AL1/72-ST1A_Verbund_SPSc Regelbauweise	Objekt KETTEN . .	Ausgabedatum 13.11.2024 Fremdnummer Blatt