


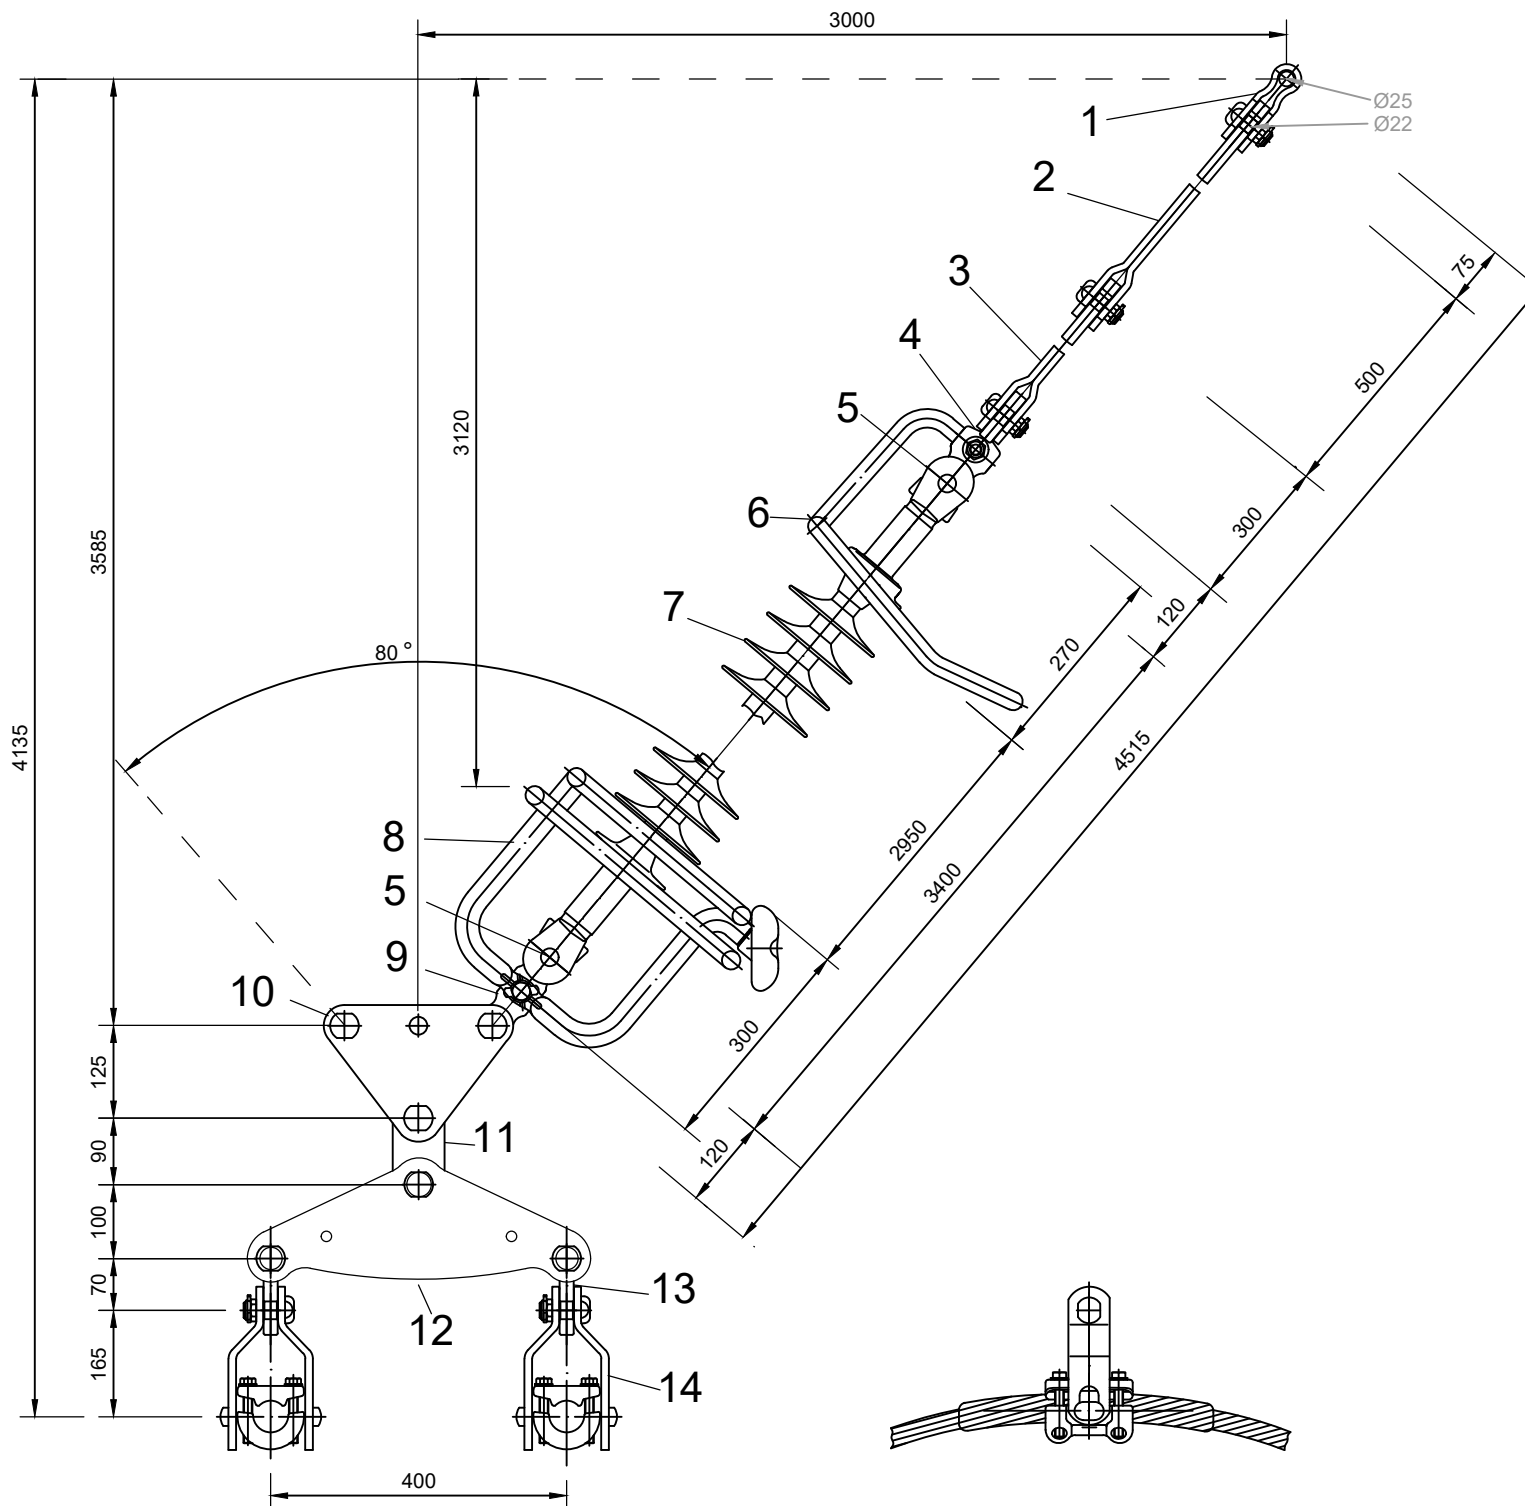

Stückliste

Pos. Nr.	Stück je Kette	Benennung	Nennkraft in kN	SAP - Nummer
1	2	Traggelenk DIN VDE 0212-466-A25x130-22-100 5)	280	52231524
2	2	Gabellasje DIN VDE 0212-478-A22-24 BH: 500	280	52223444
3	2	Gabellasje DIN VDE 0212-478-A22-24 BH: 300	280	52223440
4	2	Doppelöse D22 BH: 120 SAB Anschlag 41 GER	280	52219755
5	4	Verbindungsbolzen DIN VDE 0212-473-22x57-8.8	-	52232622
6	2	Schutzring Einhorn Verbund oben BH:270	-	52201011
7	2	Isolator Verbund CS260 10500/3400 S22	260	52105327
8	2	Schutzring Tandem Verbund unten BH:300	-	52201012
9	2	Doppelöse C22 BH: 120 SAB Anschlag 41	280	52219745
10	1	Abstandhalter DIN VDE 0212-470-A22-22-250/125 3eck	280	52225603
11	1	Doppelöse A22 BH: 90	280	52219146
12	1	Abstandhalter DIN VDE 0212-470-A19-22-400/100 3eck	280	52225577
13	2	Doppelöse DIN VDE 0212-469-B19 BH:70	200	52219213
14	2	Spiraltragklemme S19 32,25-33,69	150	52301725

Mechanische Werte

Kettengewicht:	ca. 135 kg
Kettenlänge:	ca. 4150 mm
Kettenfläche:	ca. 0,3 m²
Öffnungswinkel:	ca. 80°
max. Lastwinkel:	42,5°
Leiter/σ +10°C:	2x565-AL1/72-ST1A / 59 $\frac{N}{mm^2}$
Leiterdurchmesser:	32,85 mm
Eislastzone /Windzone:	E2/W4
Gewichts-/Windspannweite:	700/550 m

Elektrische Werte

Bemessungs-Kurzzeitstrom:	40 kA
Schlagweite:	2950 mm
Isolator:	Verbund-Longstabisolator
Ausführungsform:	CS260 1675/10500/3400
Kriechweg:	min. 10500 mm
Verschmutzungsgrad:	III nach DIN EN 60071-2:1997
SPS-Klasse:	d nach IEC 60815

Beachtung bei der Montage / Mengenermittlung

- 1) Verbindungsbolzen: Mutter und deren Sicherungen zum Mastschaft, zur niedrigeren Mastnummer oder nach unten
- 2) Brennstrebe: nach außen
- 3) Montage der Bauteile nach Herstellervorschrift
- 4) Montage der A2/A4 - Schraubenverbindungen gefettet
- 5) Pos.1: Traggelenk eventuell anpassen an Mastkonstruktion
- 6) Einbau und Anzahl gemäß Schwingungsstudie

Index	Ausgabedatum	Name	Änderung
Techn. Referenz AMG-AC-OL Dörr		erstellt von GFG-DD-DO Penning	geprüft von GFG-ON-SL Alex Schmidt
Eigentümer der Zeichnung 		Zugehörigkeit Entwurfsplanung	Erstelldatum 15.12.2025
Dokumententart Anordnungszeichnung		Status Freigegeben	Format A3-Q Maßstab -
Titel Kettenzeichnung 380-kV_V-Kette_2x565-AL1/72-ST1A_Verbund_SPSd 380-kV Audorf_Süd - Handewitt		Objekt LH-13-305	Ausgabedatum 15.12.2025
Identnummer 002-442-214		Fremdnummer	Blatt